

This drawing is the copyright of **Arid design ltd** and may not be altered or reproduced in any way without written permission

Written dimensions to be used at all times. All dimensions to be checked on site by Contractor before commencement of the works.

This drawing is to be read in conjunction with all other relevant Consultants drawings, any discrepancy to be raised prior to commencement.




External Cladding to be feather edge Cedar or Larch timber cladding painted black. Windows and doors to be Anthracite Aluminium




North Entrance to be oak frame internally with direct glazing glass, as per image.



Low level plinth to be Purbeck White Stone

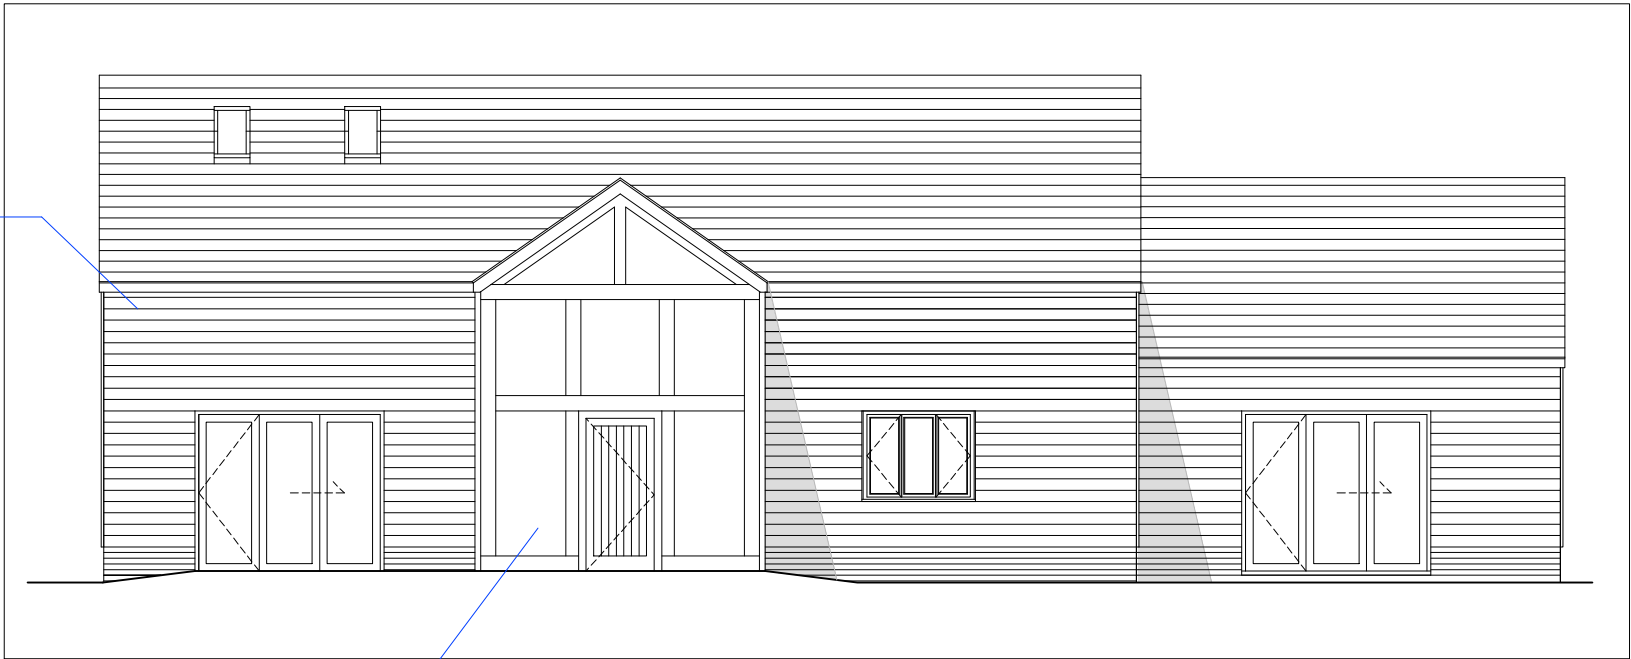


Proposed North Elevation

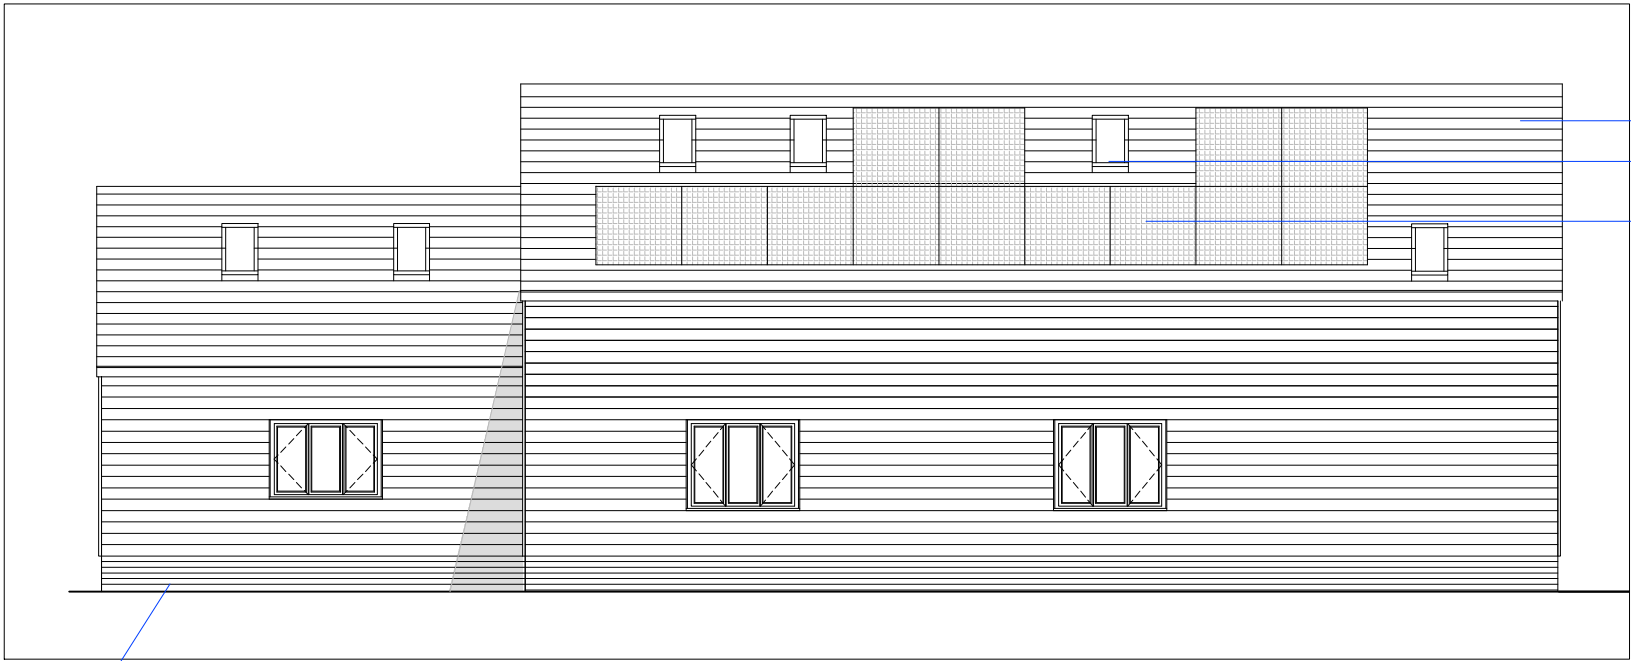

Proposed South Elevation

- Natural Slate Roof
- Grey Aluminium Roof Windows
- Photovoltaic Panels

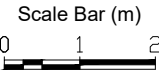

ARID

DESIGN & MANAGEMENT
Consultants

ARID Design Ltd
Tel: 01983 529895
E-mail: info@arid.uk.com

Rev A: Planning Submission

Aug 2025

Client: Mr Fairclough

Project: Land Adjacent 3 Brickfields Cottages,
East Cowes Rd, Newport, IOW

Drawing: Proposed North and South Elevations

Dwg No: 398-04

Scale: 1:100 @A3

Rev: A

Date: July 2025