



Land off Sladbury's Lane, Holland-on-Sea, Essex

Transport Statement

June 2025



STANFORDS
ESTABLISHED 1879

Document:	Transport Statement
Project:	Land off Sladbury's Lane, Holland-on-Sea, Essex
Client:	Stanfords
Job Number:	24154

Issue	Date	Status	Prepared	Reviewed	Approved
1	June 2025	Draft	MV	JP	JP
2	June 2025	FINAL	MV	JP	JP

This report has been prepared by KMC Transport Planning Ltd ('KMC') on behalf of its client to whom this report is addressed ('Client') in connection with the project described in this report and takes into account the Client's particular instructions and requirements. This report was prepared in accordance with the professional services appointment under which KMC was appointed by its Client. This report is not intended for and should not be relied on by any third party (i.e. parties other than the Client). KMC accepts no duty or responsibility (including in negligence) to any party other than the Client and disclaims all liability of any nature whatsoever to any such party in respect of this report.

Contents

1	Introduction	3
1.1	Background.....	3
1.2	Site Location	3
1.3	Report Structure	4
2	Policy Context and Guidance	5
2.1	Introduction	5
2.2	National Policy and Guidance.....	5
2.3	Local Policy and Guidance.....	6
3	Existing Conditions	11
3.1	Introduction	11
3.2	Existing Site	11
3.3	Active Travel Accessibility.....	11
3.4	Public Transport Accessibility.....	15
3.5	Local Highway Network.....	16
3.6	Road Safety	17
3.7	Local Travel Patterns	17
4	Development Proposals	19
4.1	Introduction	19
4.2	Development Quantum	19
4.3	Access Strategy	20
4.4	Parking Strategy	20
4.5	Refuse and Servicing Strategy	21
5	Trip Generation	22
5.1	Introduction	22
5.2	Vehicle Trip Rates.....	22
5.3	Forecast Vehicle Trip Generation.....	22
5.4	Summary.....	23
6	Summary and Conclusions	24
6.1	Summary.....	24
6.2	Conclusions.....	24

Figures

Figure 1.1: Site Location	3
Figure 3.1: 10-Minute Walking Catchment.....	12
Figure 3.2: 30-Minute Walking Catchment	13
Figure 3.3: 15-Minute Cycling Catchment.....	14
Figure 3.4: National Cycle Route 150 (OS Maps)	15
Figure 3.5: PIC Data Plan (31 st March 2020-31 st March 2025).....	17
Figure 4.1: Proposed Site Layout	19

Tables

Table 2.1: Essex Parking Guidance – Residential Car Parking Standards.....	9
Table 2.2: Essex Parking Guidance – Residential EV Standards.....	9
Table 2.3: Essex Parking Guidance -Residential Cycle Parking Standards.....	9
Table 3.1: Sladbury's Lane Bus Stop – Summary of Bus Services.....	15
Table 3.2: Clacton-On-Sea – Summary of Railway Services.....	16
Table 3.3: PIC Data Summary (31 st March 2020-31 st March 2025)	17
Table 3.4: Journey To Work Mode Share – Tendring 014	18
Table 4.1: Development Quantum – Summary	19
Table 5.1: Vehicle Trip Rates (per dwelling)	22
Table 5.2: Forecast Vehicle Trip Generation	22

Appendices

Appendix A	Proposed Site Layout
Appendix B	Site Access Plan
Appendix C	TRICS Data

1 INTRODUCTION

1.1 Background

- 1.1.1 KMC Transport Planning (KMC) has been appointed by Stanfords to provide transport advice in support of a planning application for the proposed development of 29No. residential dwellings (Use Class C3) on Land off Sladbury's Lane, Holland-on-Sea, Essex.
- 1.1.2 The application site is situated within the administrative boundaries of Tendring District Council (TDC), as the Local Planning Authority (LPA), and Essex County Council (ECC) as the local highway authority.

1.2 Site Location

- 1.2.1 The site is located on Land off Sladbury's Lane, within Holland-on-Sea, Essex. Holland-on-Sea is located approximately 1.5km east of the town of Clacton-on-Sea. The location of the application site in a local context is shown in **Figure 1.1**.

Figure 1.1: Site Location



- 1.2.2 The full application red line boundary is shown on the proposed site layout, contained within **Appendix A**.

1.3 Report Structure

1.3.1 This Transport Statement has been prepared in accordance with local policy and guidance as well as in reference to national policy and guidance. It should be read in conjunction with all other supporting documentation associated with the planning application.

1.3.2 The remainder of this report is structured as follows:

- Section 2: Policy Context and Guidance;
- Section 3: Existing Conditions;
- Section 4: Development Proposals;
- Section 5: Trip Generation Assessment; and
- Section 6: Summary and Conclusions.

2 POLICY CONTEXT AND GUIDANCE

2.1 Introduction

- 2.1.1 This section of the report summarises the relevant national and local policy in the context of the site and the proposed development.

2.2 National Policy and Guidance

National Planning Policy Framework (December 2024)

- 2.2.1 The National Planning Policy Framework (NPPF) sets out the Government's planning policies for England and how these are expected to be applied. Section 9 outlines the national policy on promoting sustainable transport.
- 2.2.2 Paragraph 109 highlights the importance of adopting "a vision-led approach" from the early stages of the planning process to "identify transport solutions that deliver well-designed, sustainable and popular places." To achieve this, the planning process should involve:
- *"Making transport considerations an important part of early engagement with local communities;*
 - *ensuring patterns of movement, streets, parking and other transport considerations are integral to the design of schemes, and contribute to making high quality places;*
 - *understanding and addressing the potential impacts of development on transport networks;*
 - *realising opportunities from existing or proposed transport infrastructure, and changing transport technology and usage – for example in relation to the scale, location or density of development that can be accommodated;*
 - *identifying and pursuing opportunities to promote walking, cycling and public transport use; and*
 - *identifying, assessing and taking into account the environmental impacts of traffic and transport infrastructure – including appropriate opportunities for avoiding and mitigating any adverse effects, and for net environmental gains."*
- 2.2.3 Paragraph 110 indicates that developments should be focused on locations where the need to travel can be limited and a 'genuine choice of transport modes' is available. It is recognised that these opportunities will vary between urban and rural areas, and this should be accounted for in the plan-making process.
- 2.2.4 Paragraph 115 emphasises that new developments should ensure that:
- *"Sustainable transport modes are prioritised taking account of the vision for the site, the type of development and its location;*
 - *safe and suitable access to the site can be achieved for all users;*
 - *the design of streets, parking areas, other transport elements and the content of associated standards reflects current national guidance, including the National Design Guide and the National Model Design Code; and*

- *any significant impacts from the development on the transport network (in terms of capacity and congestion), or on highway safety, can be cost effectively mitigated to an acceptable degree through a vision-led approach."*

National Planning Practice Guidance

- 2.2.5 Following the withdrawal in October 2014 of The Department for Transport (DfT) 'Guidance on Transport Assessment' (March 2007), the DfT published the Planning Practice Guidance (NPPG) suite of guidance, which is continually being updated. This guidance is intended to assist all stakeholders in determining whether an assessment may be required and, if so, what level and scope that assessment should include.
- 2.2.6 The "Travel Plans, Transport Assessments and Statements" section of NPPG was last updated in March 2014 and summarises what these documents are and how they relate to each other. It goes on to summarise the key principles of a Travel Plan, Transport Assessment and Transport Statement and what should be included in them.

2.3 Local Policy and Guidance

Essex Transport Strategy: The Local Transport Plan (2011)

- 2.3.1 The Essex Transport Strategy is the "long-term approach for transport in Essex" and emphasises their "aspirations for improving travel in the county, demonstrating the importance of meeting these aspirations to achieving sustainable long-term economic growth."
- 2.3.2 The transport vision for Essex is as follows:
- "A transport system which supports sustainable economic growth and helps deliver the best quality of life for the residents of Essex."*
- 2.3.3 To help facilitate this vision, Essex has identified five key outcomes which it aims to achieve. These are to:
- *"Provide connectivity for Essex communities and international gateways to support sustainable economic growth and regeneration;*
 - *reduce carbon dioxide emissions and improve air quality through lifestyle changes, innovation and technology;*
 - *improve safety on the transport network and enhance and promote a safe travelling environment;*
 - *secure and maintain all transport assets to an appropriate standard and ensure that the network is available for use; and*
 - *provide sustainable access and travel choice for Essex residents to help create sustainable communities."*
- 2.3.4 Policy 2 (Integrated Planning) aims to ensure that all new developments are in a sustainable location and make sure that they have the best links to public transport as well as key services to promote sustainable forms of transport.

- 2.3.5 Policy 7 (Carbon Reduction) is linked to policy 2 as it seeks to minimise all trips made by the private car by promoting the use of sustainable transport which is expanded more in Policy 8.
- 2.3.6 Policy 8 (Promoting Sustainable Travel Choices) supports sustainable transport choices by *"requiring effective travel planning for proposed developments in line with the Council's current development management policies"*.
- 2.3.7 Policy 10 (Road Safety) is a measure to ensure that priorities strategies and proposals that will reduce the number of people injured or killed on the roads.
- 2.3.8 Policy 14 (Cycling) is dedicated to making sure that everyone is aware of the benefits of cycling and encouraging it by improving and developing the cycle infrastructure within the county, as well as providing training opportunities for all.
- 2.3.9 Policy 15 (Walking and Public Rights of Way) has the same focus as Policy 14 but aimed at walking rather than cycling. The benefits of walking it to be promoted as well as ensuring that the environment is safe and conducive for pedestrians.

Tendring District Local Plan Part 1 (2021) and Part 2 (2022)

- 2.3.10 The adopted Tendring District Local Plan (hereby referred to as the 'Local Plan') sets out how development in Tendring can best benefit the district. The current adopted Tendring District Local Plan is formed of two sections, as follows:
- Section 1 - Tendring District Local Plan 2013-2033 and Beyond (adopted January 2021); and
 - Section 2 – Tendring District Local Plan 2013-2033 and Beyond: Section 2 (adopted January 2022).
- 2.3.11 Due to the strategical and functional relationships, as well as the strategic-cross boundary policies and allocations, the districts of Tendring, Colchester and Braintree share an 'identical' Section 1 of their Local Plans.

Part 1 - Tendring District Local Plan 2013-2033 and Beyond (adopted January 2021)

- 2.3.12 Section 1 of the adopted Local Plan details policies that are applicable to all three districts, including Tendring.
- 2.3.13 Local Plan Policy SP7 "Creating Quality Places" is of relevance to the site from a transport perspective. This policy states that all new development should:
- Create well-connected places that prioritise the needs of pedestrians, cyclists and public transport services above use of the private car;
 - Provide streets and spaces that are overlooked and active and promote inclusive access; and
 - Include parking facilities that are well integrated as part of the overall design and are adaptable if levels of private car ownership fall.

Part 2 – Tendring District Local Plan 2013-2033 and Beyond (adopted January 2022)

- 2.3.14 Section 2 of the Local Plan highlights the specific vision, objectives and policies for the Tendring District. The overarching vision of the Local Plan is as follows:

"In 2033, Tendring District will be a vibrant, healthy and attractive place to live, work and visit. It will have a thriving, resilient and prosperous economy that promotes sustainable economic growth, making sustainable use of its natural and historic environments, maritime connections and popularity as a visitor destination"

- 2.3.15 The overarching vision is supported by ten strategic sub-objectives. Objective Four 'Infrastructure Provision' is of relevance to the proposed development from a transport perspective, stating the district should *"make efficient use of existing transport infrastructure and ensure sustainable transport opportunities are promoted in all new development. Where additional capacity is required in the form of new or upgraded transport infrastructure, to ensure this is provided as necessary in connection with new development"*. There are a range of policies that support the vision and sub-objectives of the Local Plan.
- 2.3.16 **Policy CP1** requires new developments to promote sustainable transport—walking, cycling, and public transport—particularly for major projects like those in Clacton and the Tendring Colchester Borders Garden Community. Major developments must submit a Transport Statement or Assessment, agreed with the Council and Essex County Council.
- 2.3.17 **Policy CP2** supports developments that enhance a safe, efficient, and sustainable transport system. Planning permission will be refused if a proposal causes unacceptable highway safety issues or severe impacts on the road network.

Essex County Council Parking Guidance (2024)

- 2.3.18 The Essex Parking Guidance was published in December 2024 and provides the guidance for new developments in the county. The guidance looks at solutions to accommodate parking for a range of vehicles and proposed a level of provision which balance demand/provision with the need to create quality public/private spaces.

Car Parking

- 2.3.19 The residential car parking standards contained within the Essex Parking Guidance are shown in **Table 2.1**. These standards are based upon an area's 'connectivity' rating, contained within the guidance. The location of the proposed development is reported to be in an area of 'good' connectivity.

Table 2.1: Essex Parking Guidance – Residential Car Parking Standards

Number of bedrooms	Vehicle	PTW	Disabled
1 bedroom	1 + 0.25 unallocated visitor	N/A	
2 bedrooms	2 + 0.25 unallocated visitor	For unallocated/ visitor provision: 1 space + 1 space per 20 car spaces for first 100 car spaces, then 1 space per 30 car spaces over 100 car spaces	N/A if parking is in curtilage of dwelling
3 bedrooms			
4 + bedrooms			

2.3.20 The parking standards for Electric Vehicle (EV) provision are also shown in **Table 2.2**.

Table 2.2: Essex Parking Guidance – Residential EV Standards

Type of Development	EV Parking Standard
C3 – Dwelling Houses	For every dwelling with allocated car parking, at least one parking space shall be provided with an active EV charge point. Remaining on-street, shared, or visitor spaces shall be provided with an active EV charge point at a ratio of 1 in 5. All remaining spaces shall have passive provision.
C3 – Dwelling Apartments (with less than 10 associated parking spaces)	
C3 – Dwelling Apartments (with more than 10 associated parking spaces)	

Cycle Parking

2.3.21 Essex Parking Guidance (2024) also contains standards for cycle parking at new residential developments. The standards are expressed as minimums. The standards extracted from Essex Parking Guidance are shown in **Table 2.3**.

Table 2.3: Essex Parking Guidance -Residential Cycle Parking Standards

Development Type	Short Stay / Visitor	Long Stay / Resident
C3 – Residential Dwellings	1 space per 40 dwellings. This is complementary to any additional parking that is provided by local authorities. A minimum of 10% of the total cycle parking spaces are required to be designed with non-standard bicycles in mind/	1 space per bedroom (if no garage or secure area is provided in curtilage of dwelling) A minimum of 10% of the total cycle parking spaces are required to be designed with non-standard bicycles in mind.

- 2.3.22 The guidance also states that cycle parking should be provided on-site, within close proximity to the origin and destination of trips in a secure and covered location.

3 EXISTING CONDITIONS

3.1 Introduction

3.1.1 This section of the report outlines the existing transport context in relation to the site.

3.2 Existing Site


3.2.1 The application site is currently vacant land located off Sladbury's Lane, Holland-on-Sea. The site is bound by Sladbury's Lane to the east/south, agricultural land to the north and the rear of residential properties located off Maris Otter Lane to the west. The neighbouring residential properties to the west off Maris Otter Lane are recently constructed and were approved as part of a wide planning application (reference 15/01351/OUT and 20/01416/DETAIL) for *"up to 132 dwellings and open space, including provision for a sports field and a new vehicular access via Sladbury's Lane"*. This application included the provision of a highway improvements, such as the Sladbury's Lane (N) / Edward Giles Way / Sladbury's Lane (S) roundabout and section of footway on the western side of Sladbury's Lane.

3.3 Active Travel Accessibility

Walking


3.3.1 The National Design Guide (2021) refers to a single common walkable distance of approximately 800m, which is equivalent to an approximate 10-minute walk. However, destinations outside this catchment may still be achievable to many. **Figure 3.1** illustrates the 10-minute walking isochrone from the application site, which equates to an approximate 800m walk.

Figure 3.1: 10-Minute Walking Catchment

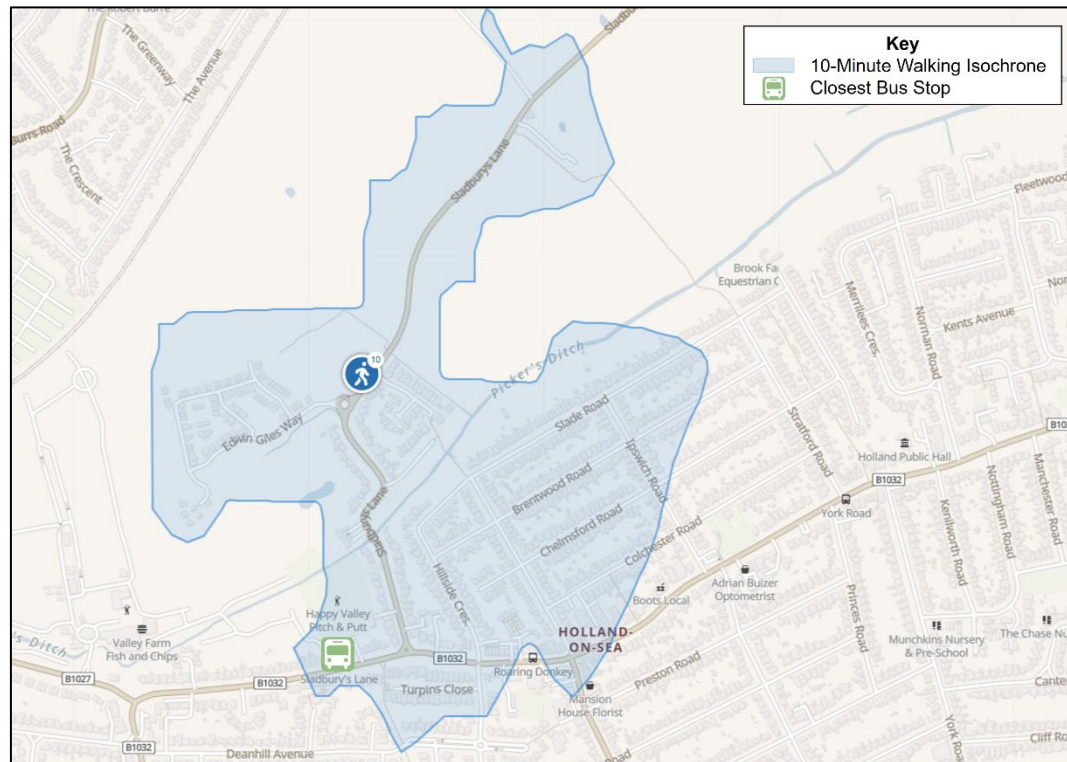

- 3.3.2 **Figure 3.1** illustrates that an area of Holland-on-Sea is accessible from the site within an approximate 10-minute walking distance. This includes the Sladbury's Lane Bus Stop (further detailed in **Section 3.4**). In the vicinity of the application site, there is existing footway provision adjacent to the eastern side of Sladbury's Lane that provides a southbound connection to Holland Road. Streetlighting is also provided.
- 3.3.3 To highlight what facilities, services and amenities may be accessible further than a 10-minute walking distance from the application site. **Figure 3.2** provides the 30-minute walking catchment from the application site.

Figure 3.2: 30-Minute Walking Catchment

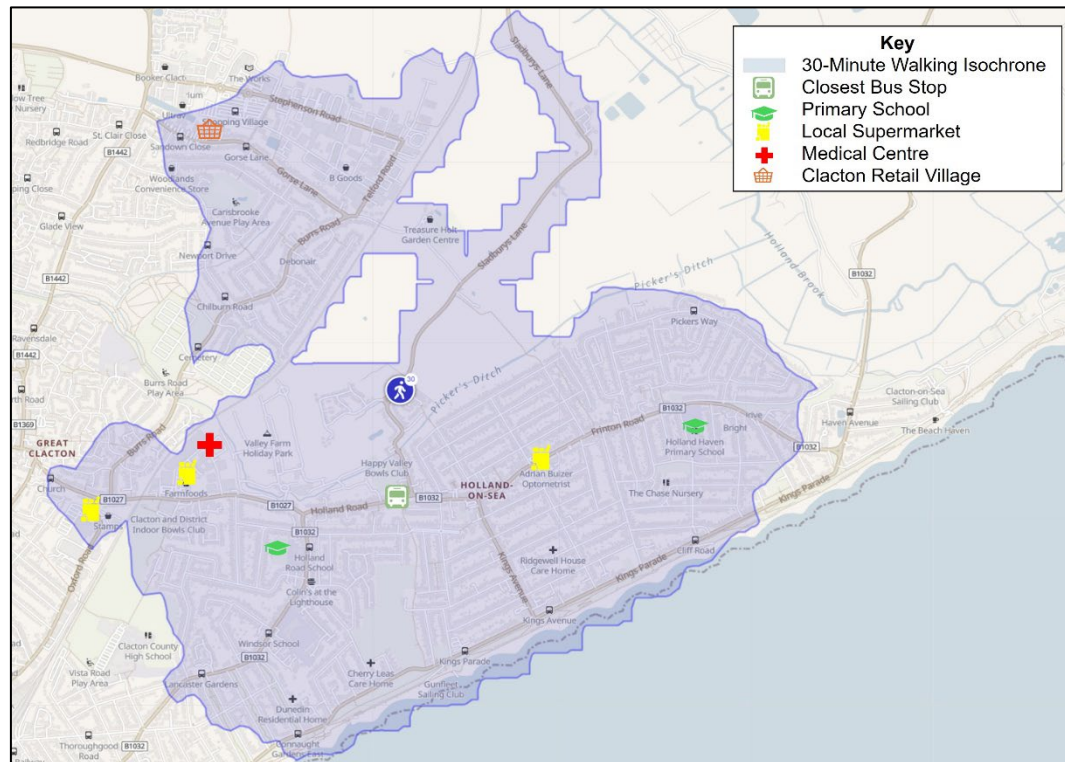


- 3.3.4 **Figure 3.2** shows that there are a number of amenities, facilities and services within a 30-minute walking catchment of the application site. This includes a number of primary schools, local supermarkets, a medical centre and Clacton Retail Village.

Cycling


- 3.3.5 Cycling has the potential to substitute for short car trips, particularly those under 5km. **Figure 3.3** shows the 15-minute cycling isochrone from the application site, which equates to an approximately 5.0km cycle ride.

Figure 3.3: 15-Minute Cycling Catchment

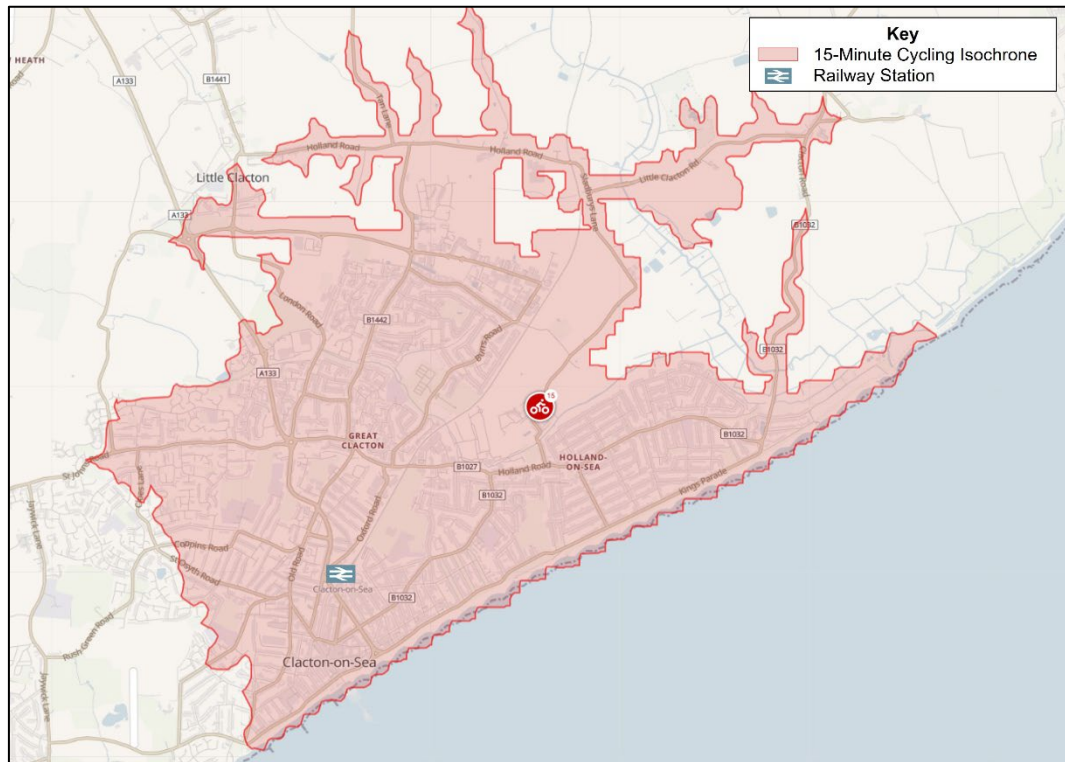

- 3.3.6 **Figure 3.3** shows that within a 15-minute cycle ride of the application site, all of Clacton-on-Sea is accessible. This includes Clacton-on-Sea Railway Station (further detailed in **Section 3.4**), as well as the range of town-centre facilities and amenities and day-to-day services. The majority of roads within Clacton-on-Sea are subject to a 30mph posted speed limit, which is considered to be conducive to cycling.
- 3.3.7 The application site is also located approximately 1.0km north of National Cycle Route 150, which forms part of the Sustrans National Cycle Network (NCN). Route 150 is a coastal cycle road that runs between Walton-on-the-Naze to the north, and Clacton-on-Sea to the south via Frinton-on-Sea. **Figure 3.4** illustrates the National Cycle Route 150.

Figure 3.4: National Cycle Route 150 (OS Maps)

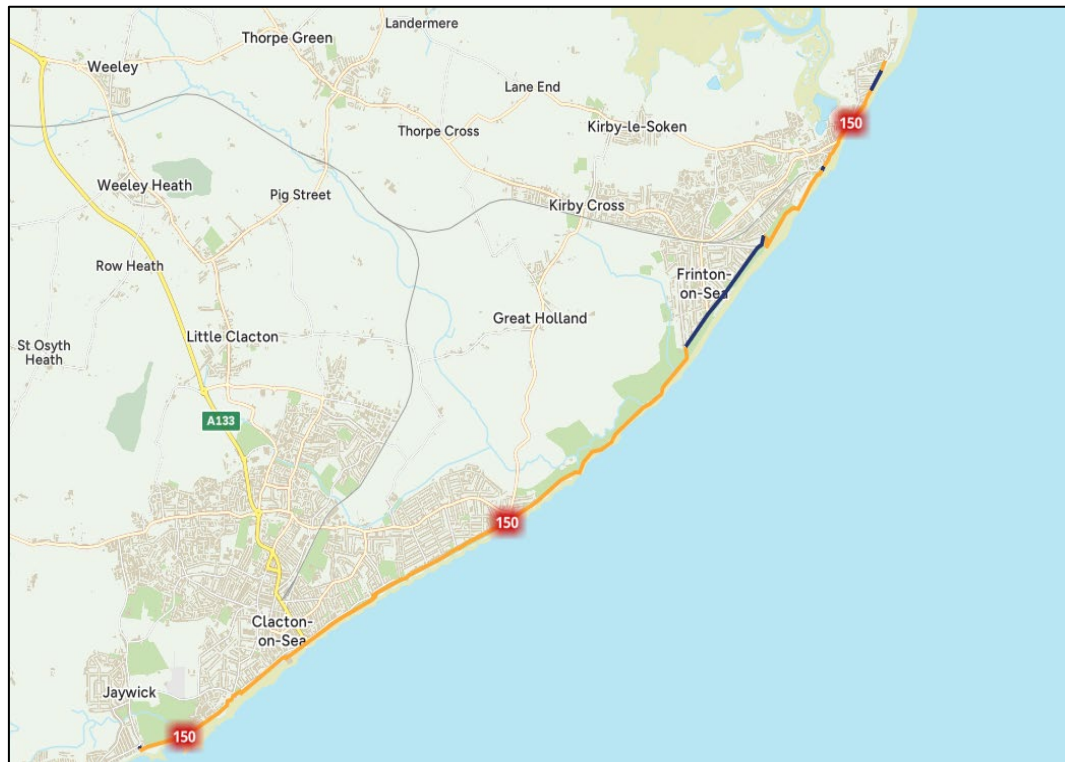

3.4 Public Transport Accessibility

Bus

- 3.4.1 The nearest bus stops to the site are located on Holland Road, located approximately 700m to the south via Sladbury's Lane. The Bus Stops, known as the 'Sladbury's Lane Bus Stop', are flagged with timetable information and kerbside provision.
- 3.4.2 A summary of the bus services operating from the Sladbury's Lane Bus Stop is provided in **Table 3.1** below.

Table 3.1: Sladbury's Lane Bus Stop – Summary of Bus Services

Service	Route	Peak Frequency			First / Last Service		
		Weekday	Sat.	Sun.	Weekday	Sat.	Sun.
7	Clacton to Walton on the Naze	4 buses per hour	3 buses per hour	1 bus per hour	06:33/ 19:23	07:08/ 19:23	09:41/ 17:46
98A	Clacton to Walton on the Naze	2 buses per day	2 buses per day	-	20:23/ 21:58	20:23/ 21:58	-

- 3.4.3 **Table 3.1** illustrates that there are frequent bus services operating from the Sladbury's Lane Bus Stop, which provide services to destinations such as Clacton Town Centre, Clacton Railway Station, Frinton-On-Sea, and Walton-on-the-Naze.

Rail

- 3.4.4 The closest railway station to the site is the 'Clacton-On-Sea' Railway Station, located approximately 2.7km southwest, or an approximate 11-minute cycle-ride or 4-minute bus journey.
- 3.4.5 Clacton-On-Sea Railway Station is situated on the Sunshine Coast Line. A summary of the railway services that operate from here is provided in **Table 3.2**. All services are operated by Abilo Greater Anglia.

Table 3.2: Clacton-On-Sea – Summary of Railway Services

Destination	Approx. Journey Time	Peak Frequency
London Liverpool Street	90 Minutes	2 services per hour

- 3.4.6 Trains also stop at a range of intermediate railway stations, including, but not limited to:
- Colchester;
 - Witham;
 - Chelmsford;
 - Hatfield Peverel; and
 - Stratford.


3.5 Local Highway Network

- 3.5.1 The application site is located off Sladbury's Lane, adjacent to the western side of the carriageway. Sladbury's Lane is a single carriageway road with a posted speed limit of 30mph in the immediate vicinity of the application site.
- 3.5.2 To the south of the application site, Sladbury's Lane continues for approximately 60m before forming a three-armed roundabout with Edwins Giles Way and Sladbury's Lane (S). Sladbury's Lane continues south for approximately 450m and forms a priority junction with Holland Road. To the east, Holland Road provides a route into the centre of Holland-on-Sea and a connection to the B1032. To the west, Holland Road continues as B1027 and provides a connection into the centre of Clacton-on-Sea.
- 3.5.3 To the north of the application site, the posted speed limit on Sladbury's Lane changes to national speed limit approximately 30m to the north. Sladbury's Lane continues north for approximately 450m where a priority junction is formed with Burrs Road. Burrs Road runs northwest and provides a connection into North Clacton-on-Sea, via Gorse Road and Thorpe Road.

3.6 Road Safety

3.6.1 Personal Injury Collision (PIC) data has been sourced from the ECC online portal for the most readily available full 60-month (five years) period (31st March 2020-31st March 2025), for a study area that extends approximately 250m either side of the application site. The study area covers Sladbury's Lane, as well as the priority junction with Holland Road to the south. **Figure 3.5** displays the recorded PICs in plan form.

Figure 3.5: PIC Data Plan (31st March 2020-31st March 2025)

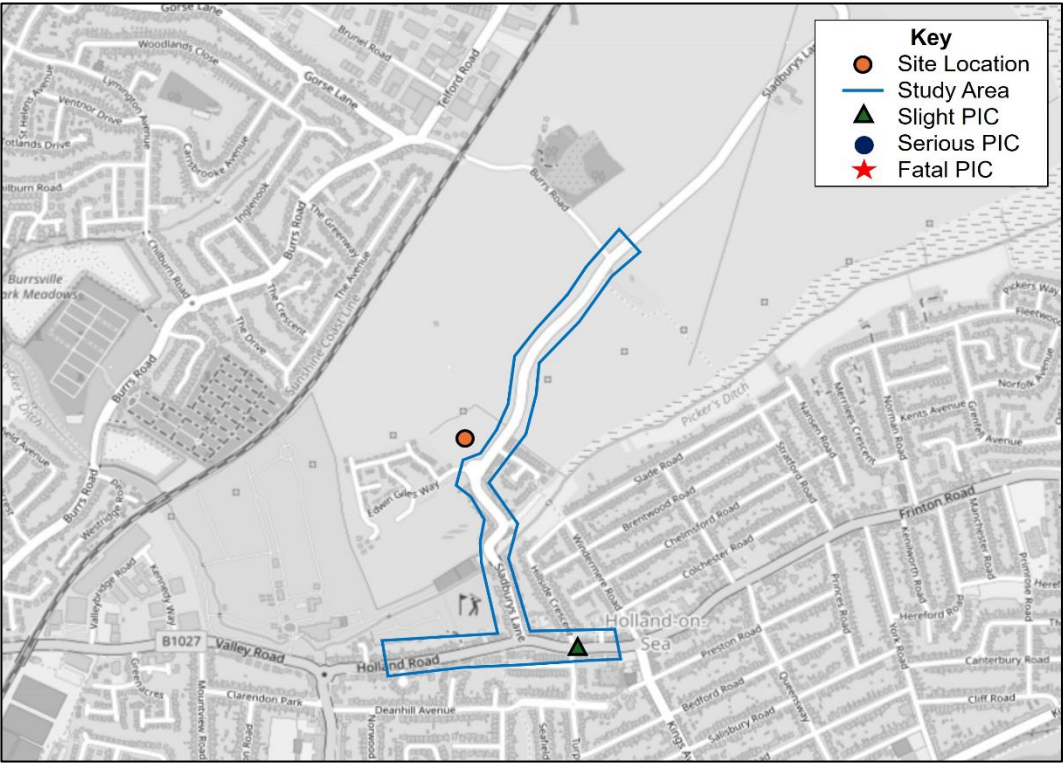

3.6.2 **Figure 3.5** shows that one PIC was recorded in the last readily available 60-month period within the study area. With regards to severity, PIC was recorded as 'slight'. A summary of the PIC is provided in **Table 3.3**.

Table 3.3: PIC Data Summary (31st March 2020-31st March 2025)

Reference	Severity	Date	Time	No. of Vehicles	No. of Casualty's	Vulnerable User Casualty
221246620	Slight	November 2022	09:37	3	1	No

3.7 Local Travel Patterns

3.7.1 To understand the existing travel patterns of the local area, the 2011 Census dataset "WU03EW - Location of usual residence and place of work by method of travel to work (MSOA level)" has been

interrogated for middle super output area (MSOA) Tendring 014 which is considered representative of the local area.

- 3.7.2 The journey to work mode share for MSOA Tendring 014 in accordance with the 2011 Census is provided in **Table 3.4**.

Table 3.4: Journey To Work Mode Share – Tendring 014

Method of travel	Mode Share
Underground, metro, light rail or tram	0%
Train	5%
Bus, minibuss or coach	2%
Taxi	0%
Motorcycle, scooter or moped	1%
Driving a car or van	60%
Passenger in a car or van	7%
Bicycle	4%
On foot	19%
Other method of travel to work	1%
Total	100%

- 3.7.3 **Table 3.4** shows that for commuting journeys in MSOA Tendring 014, 60% of residents drive their own car/van, whilst 7% are passengers in a car or van. Active travel accounts for 23% of journeys, whilst public transport accounts for 7%. Therefore, the data in **Table 3.4** illustrates that whilst 60% of residents drive their own car, 30% utilise sustainable modes of transport (public transport and active travel). 10% of residents travel by other methods.

4.3 Access Strategy

Vehicle

- 4.3.1 Vehicular access to the proposed development will be achieved through the provision of a new priority junction with Sladbury's Lane.
- 4.3.2 The full proposed site access design with Sladbury's Lane is illustrated in drawing **KMC24151/001**, which is contained within **Appendix B**. The proposed site access has been designed in accordance with the principles set out in Essex Design Guide and accords with 'Road Type E'.
- 4.3.3 Drawing **KMC24151/001** also illustrates that visibility splays of 2.4m x 43m are achievable in both directions on Sladbury's Lane, pertinent to the requirements of a 30mph road set out in Manual for Streets (MfS).

Pedestrian

- 4.3.4 Pedestrian access to the proposed development will also be achieved from Sladbury's Lane.
- 4.3.5 A new 2.0m wide pedestrian footway (as shown in drawing **KMC24251/001**) will be provided from the proposed site access south towards the Sladbury's Lane (N) / Edward Giles Way / Sladbury's Lane (S) roundabout where it will connect into the existing footway provision.
- 4.3.6 This will then provide an onwards pedestrian connection to the south to Holland-on-Sea and Clacton-on-Sea.

4.4 Parking Strategy

Car

- 4.4.1 Car parking at the proposed development will be provided in accordance with the standards relevant to the application site location detailed in the Essex Parking Guidance (2024).
- 4.4.2 Allocated car parking for each dwelling will be provided on-plot, as a driveway and/or within appropriately sized garages.
- 4.4.3 Visitor car parking will also be provided at the proposed development. This will be unallocated. A total of 7 visitor car parking spaces, located across the proposed development, are to be provided. This is in accordance with Essex Parking Guidance (2024).

Cycle

- 4.4.4 Cycle parking at the proposed development will be provided in accordance with the minimum requirements set out in Essex Parking Guidance (2024).
- 4.4.5 Cycle parking will be provided on-plot, within a secure, sheltered and convenient location. Where appropriate, cycle parking will be provided within garages of properties.

4.5 Refuse and Servicing Strategy

- 4.5.1 The internal road layout will be designed to accommodate refuse collection vehicles and fire tender access.
- 4.5.2 Bin storage will be provided in accordance with guidance on bin drag distances i.e. 30m for residents and 25m for refuse operators.

5 TRIP GENERATION

5.1 Introduction

5.1.1 This section of the report considers the forecast vehicle trip generation for the proposed 29 residential dwellings at the site.

5.2 Vehicle Trip Rates

5.2.1 The TRICS V7.11.4 database has been consulted to derive vehicle trip rates (per dwelling) for the proposed development, using the following key selection criteria:

- Land Use: 03 – Residential;
- Category: A – Houses Privately Owned;
- Location: England, excluding Greater London;
- Number of houses: 10-35 houses; and
- Survey days: Weekdays only.

5.2.2 The full selection criteria and full outputs are contained within **Appendix C**.

5.2.3 The AM peak hour and PM peak hour vehicle trip rates extracted from the TRICS database are provided below in **Table 5.1**. The peak hour trip rates for the proposed development are forecast to differ minorly between the apartments and houses. However, to provide a robust assessment, the respective peak hour of each housing type has been assessed and combined to form a worst-case assessment.

Table 5.1: Vehicle Trip Rates (per dwelling)

Housing Type	AM Peak Hour			PM Peak Hour		
	Arr.	Dep.	Two-way	Arr.	Dep.	Two-way
Vehicle Trip Rates (Per Dwelling)	0.181	0.396	0.577	0.340	0.199	0.539

5.3 Forecast Vehicle Trip Generation

5.3.1 The AM and PM peak hour vehicle trip rates (per dwelling) provided in **Table 5.1** have been applied to the proposed 29 residential dwellings at the site. The resultant forecast vehicle trip generation of the proposed development is shown in **Table 5.2**.

Table 5.2: Forecast Vehicle Trip Generation

Housing Type	AM Peak Hour			PM Peak Hour		
	Arr.	Dep.	Two-way	Arr.	Dep.	Two-way
Vehicle Trip Generation (29 houses)	5	12	17	10	6	16

- 5.3.2 **Table 5.2** shows that in the AM peak hour, the proposed development is forecast to generate a total of 17 two-way vehicle trips (5 arrivals and 12 departures). In the PM peak hour, the proposed development is forecast to generate a total of 16 two-way vehicle trips (10 arrivals and 6 departures).

5.4 Summary

- 5.4.1 The proposed development is forecast to have a negligible impact on the local highway network. In the AM peak hour and PM peak hour, the proposed development is forecast to generate one additional vehicle trip on the local highway network approximately every 4 minutes.

6 SUMMARY AND CONCLUSIONS

6.1 Summary

- 6.1.1 KMC Transport Planning has been appointed by Stanfords to prepare a Transport Statement in support of a planning application for the proposed development of 29No. residential dwellings on Land off Sladbury's Lane, Holland-on-Sea, Essex. The proposed development comprises of 21No. houses and 8No. apartments.
- 6.1.2 The application site is located within a 10-minute walking distance to the nearest bus stop, which provides connections to nearby towns and settlements in the region. There is also a range of services and amenities within walking distance of the application site. Local roads are also conducive to cycling.
- 6.1.3 Access to the proposed development will be achieved from a priority junction with Sladbury's Lane. A proposed site access drawing has been prepared by KMC which illustrates the required visibility splays can be achieved.
- 6.1.4 Car and cycle parking provision at the proposed development will be provided in accordance with the standards set out in the Essex Parking Guidance (2024) document.
- 6.1.5 A peak hour vehicle trip generation assessment demonstrates that the proposed development is forecast to generate a total of 17 two-way vehicle movements in the AM peak hour and 16 two-way vehicle movements in the PM peak hour. It is forecast that this will have a negligible impact on the operation of the local highway network.

6.2 Conclusions

- 6.2.1 In conclusion, the assessment undertaken within this Transport Statement demonstrates that the proposed development is acceptable in transport terms, and there are no highways or transport-related reasons why planning permission should not be granted.

Appendix A Proposed Site Layout



132 dwellings under
20/01416/DETAIL

ACCOMMODATION

Total 29 dwellings shown:
combination of 1 - 2.5 storey, each
with min 2 no. 5.5 x 2.9 parking
spaces.
As shown, 8 no. 2-bed apartments,
21 no. 3 beds (semi-detached,
detached - generic to allow for
adjustment)

ACCESS

New access (Minor Access Way) shown
as discussed (requires removal of Field
Maple)

Vision splay - 90m - shown pink at
entrance

Footpath shown blue line with blue
circles for links within scheme and to
adjacent green space.

LAYOUT

Storey heights as previously shown.
Development set back from Strategic
Green Gap to NE boundary, and with
active frontage.

GENERAL NOTES

1. Dimensions are in millimetres (unless stated otherwise) and are to block or stud faces.
2. Drawings are not to be scaled, use figured dimensions only.
3. Notify the Architect of any discrepancies within the drawing and contact for clarification before proceeding.
4. All proprietary items to be fitted strictly in accordance with manufacturers instructions.
5. All works to be carried out in accordance with latest related British Standards and relevant codes of practice.

Rev	Date	Revision Description
Project Title		
PROPOSED RESIDENTIAL DEVELOPMENT, LAND OFF SLADBURY'S LANE		Scale 1:500 @ A2
Project Ref.		3735
Drawing Title		Drawing Ref. PA-10-A
Date Drawn		MAY 2025
Drawn By		CR
Checked By		CR

SITE PLAN PROPOSED



DUNCAN CLARK & BECKETT LTD
12A William's Walk, Colchester, Essex, CO1 1TS




RIBA
Chartered Practice



CIAT
CHARTERED PRACTICE

Appendix B Site Access Plan

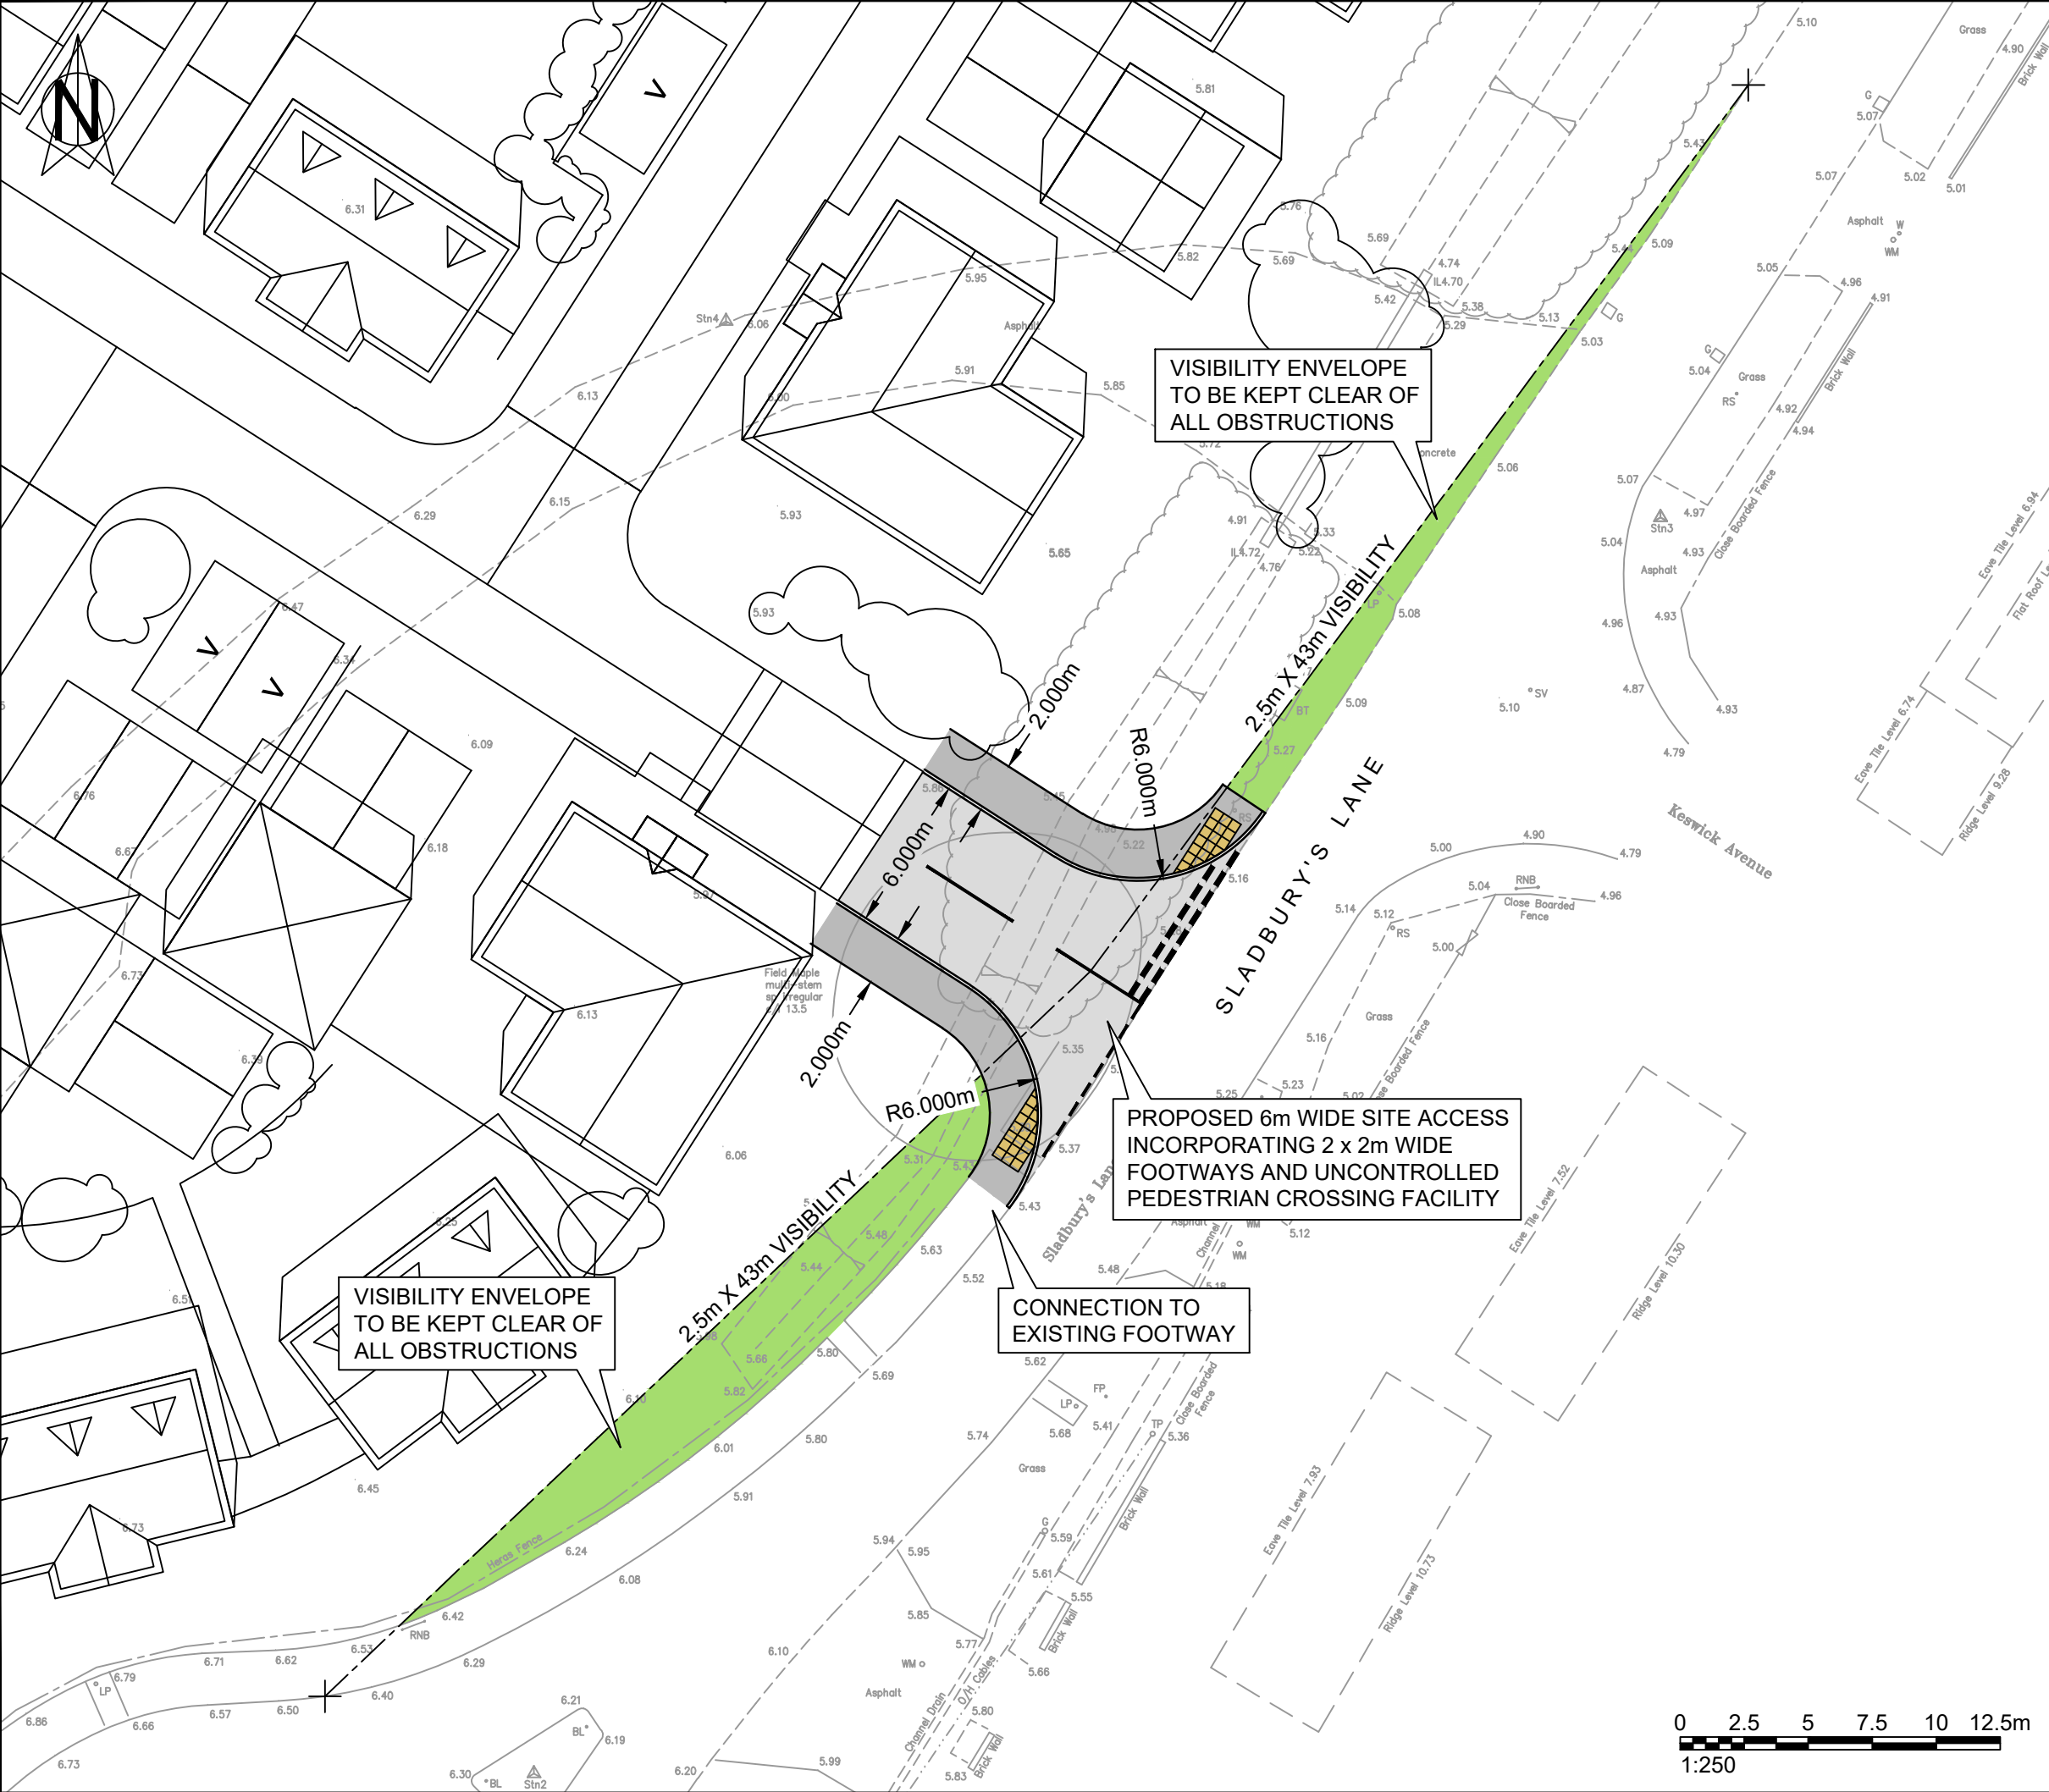

- NOTES :**
1. (C) This drawing is copyright.
 2. All dimensions to be checked on site.
 3. Do not scale from this drawing; only figured dimensions are to be worked from.
 4. Any discrepancies must be reported immediately before proceeding.
 5. This drawing to be read & printed in colour.

REV	DATE	DESCRIPTION	DRN	CHKD	APRD
...	...	...	...	...	...

Issue Status					
☐ CONCEPT	☐ PRELIMINARY	☐ TENDER	☐ CONSTRUCTION	☐ AS BUILT	☐ H&S FILE ISSUE

Client
Stanfords

Project
Land off Sladbury's Ln,
Holland-on sea, Essex

Drawing Title
Proposed Site Access

Scale @ A3 1:250	Drwn DW	Chkd JP
	Aprd KMCM	Date 18.06.2025

Drawing Ref KMC24154 / 001	Rev
-------------------------------	-----

kmc
transport planning

Appendix C TRICS Data

Calculation Reference: AUDIT-805401-250613-0628

TRIP RATE CALCULATION SELECTION PARAMETERS:

Land Use : 03 - RESIDENTIAL
 Category : A - HOUSES PRIVATELY OWNED
 TOTAL VEHICLES

Selected regions and areas:

02	SOUTH EAST	
	BO BEDFORD	1 days
	ES EAST SUSSEX	1 days
	KC KENT	1 days
	MW MEDWAY	1 days
	SC SURREY	1 days
03	SOUTH WEST	
	DC DORSET	1 days
04	EAST ANGLIA	
	CA CAMBRIDGESHIRE	1 days
	NF NORFOLK	1 days
	SF SUFFOLK	1 days
06	WEST MIDLANDS	
	ST STAFFORDSHIRE	1 days
07	YORKSHIRE & NORTH LINCOLNSHIRE	
	BY BARNSLEY	1 days
	SE SHEFFIELD	1 days
08	NORTH WEST	
	LC LANCASHIRE	1 days
09	NORTH	
	IM ISLE OF MAN	2 days

This section displays the number of survey days per TRICS® sub-region in the selected set

Primary Filtering selection:

This data displays the chosen trip rate parameter and its selected range. Only sites that fall within the parameter range are included in the trip rate calculation.

Parameter: No of Dwellings
 Actual Range: 12 to 34 (units:)
 Range Selected by User: 10 to 35 (units:)

Parking Spaces Range: All Surveys Included

Parking Spaces per Dwelling Range: All Surveys Included

Bedrooms per Dwelling Range: All Surveys Included

Percentage of dwellings privately owned: All Surveys Included

Public Transport Provision:

Selection by: Include all surveys

Date Range: 01/01/16 to 18/09/24

This data displays the range of survey dates selected. Only surveys that were conducted within this date range are included in the trip rate calculation.

Selected survey days:

Monday	1 days
Tuesday	1 days
Wednesday	8 days
Thursday	4 days
Friday	1 days

This data displays the number of selected surveys by day of the week.

Selected survey types:

Manual count	14 days
Directional ATC Count	1 days

This data displays the number of manual classified surveys and the number of unclassified ATC surveys, the total adding up to the overall number of surveys in the selected set. Manual surveys are undertaken using staff, whilst ATC surveys are undertaken using machines.

Selected Locations:

Edge of Town	7
Neighbourhood Centre (PPS6 Local Centre)	8

This data displays the number of surveys per main location category within the selected set. The main location categories consist of Free Standing, Edge of Town, Suburban Area, Neighbourhood Centre, Edge of Town Centre, Town Centre and Not Known.

Selected Location Sub Categories:

Residential Zone	7
Village	8

This data displays the number of surveys per location sub-category within the selected set. The location sub-categories consist of Commercial Zone, Industrial Zone, Development Zone, Residential Zone, Retail Zone, Built-Up Zone, Village, Out of Town, High Street and No Sub Category.

Inclusion of Servicing Vehicles Counts:

Servicing vehicles Included	X days - Selected
Servicing vehicles Excluded	15 days - Selected

Secondary Filtering selection:**Use Class:**

C3	15 days
----	---------

This data displays the number of surveys per Use Class classification within the selected set. The Use Classes Order (England) 2020 has been used for this purpose, which can be found within the Library module of TRICS®.

Population within 500m Range:

All Surveys Included

Secondary Filtering selection (Cont.):

Population within 1 mile:

1,001 to 5,000	8 days
5,001 to 10,000	1 days
10,001 to 15,000	5 days
20,001 to 25,000	1 days

This data displays the number of selected surveys within stated 1-mile radii of population.

Population within 5 miles:

5,000 or Less	1 days
5,001 to 25,000	2 days
25,001 to 50,000	4 days
50,001 to 75,000	1 days
75,001 to 100,000	1 days
100,001 to 125,000	1 days
125,001 to 250,000	4 days
500,001 or More	1 days

This data displays the number of selected surveys within stated 5-mile radii of population.

Car ownership within 5 miles:

0.6 to 1.0	3 days
1.1 to 1.5	10 days
1.6 to 2.0	2 days

This data displays the number of selected surveys within stated ranges of average cars owned per residential dwelling, within a radius of 5-miles of selected survey sites.

Travel Plan:

Yes	6 days
No	9 days

This data displays the number of surveys within the selected set that were undertaken at sites with Travel Plans in place, and the number of surveys that were undertaken at sites without Travel Plans.

PTAL Rating:

No PTAL Present	15 days
-----------------	---------

This data displays the number of selected surveys with PTAL Ratings.

Covid-19 Restrictions	Yes	At least one survey within the selected data set was undertaken at a time of Covid-19 restrictions
-----------------------	-----	--

LIST OF SITES relevant to selection parameters

1	BO-03-A-01 CARNOUSTIE DRIVE BEDFORD GREAT DENHAM Edge of Town Residential Zone Total No of Dwellings: 30 Survey date: THURSDAY 15/10/20	DETACHED HOUSES BEDFORD	Survey Type: MANUAL
2	BY-03-A-01 CHURCH LANE NEAR BARNESLEY WORSBROUGH Neighbourhood Centre (PPS6 Local Centre) Village Total No of Dwellings: 19 Survey date: WEDNESDAY 09/09/20	BUNGALOWS & DETACHED BARNESLEY	Survey Type: MANUAL
3	CA-03-A-07 FIELD END NEAR ELY WITCHFORD Neighbourhood Centre (PPS6 Local Centre) Village Total No of Dwellings: 32 Survey date: THURSDAY 27/05/21	MIXED HOUSES CAMBRIDGESHIRE	Survey Type: MANUAL
4	DC-03-A-10 ADDISON CLOSE GILLINGHAM Edge of Town Residential Zone Total No of Dwellings: 26 Survey date: WEDNESDAY 09/11/22	MIXED HOUSES DORSET	Survey Type: MANUAL
5	ES-03-A-06 BISHOPS LANE RINGMER Neighbourhood Centre (PPS6 Local Centre) Village Total No of Dwellings: 12 Survey date: WEDNESDAY 16/06/21	MIXED HOUSES EAST SUSSEX	Survey Type: MANUAL
6	IM-03-A-01 BALLAKILLOWEY ROAD COLBY BALLAKILLOWEY Neighbourhood Centre (PPS6 Local Centre) Village Total No of Dwellings: 31 Survey date: TUESDAY 21/05/24	MIXED HOUSES ISLE OF MAN	Survey Type: MANUAL
7	IM-03-A-02 SHORE ROAD KIRK MICHAEL Neighbourhood Centre (PPS6 Local Centre) Village Total No of Dwellings: 27 Survey date: THURSDAY 23/05/24	MIXED HOUSES ISLE OF MAN	Survey Type: MANUAL
8	KC-03-A-09 WESTERN LINK FAVERSHAM DAVINGTON Edge of Town Residential Zone Total No of Dwellings: 14 Survey date: WEDNESDAY 09/06/21	MIXED HOUSES & FLATS KENT	Survey Type: MANUAL

LIST OF SITES relevant to selection parameters (Cont.)

9	LC-03-A-31 GREENSIDE PRESTON COTTAM Edge of Town Residential Zone Total No of Dwellings: 32 Survey date: FRIDAY 17/11/17	DETACHED HOUSES	LANCASHIRE	Survey Type: MANUAL
10	MW-03-A-02 OTTERHAM QUAY LANE RAINHAM Edge of Town Residential Zone Total No of Dwellings: 19 Survey date: MONDAY 06/06/22	MIXED HOUSES	MEDWAY	Survey Type: MANUAL
11	NF-03-A-10 HUNSTANTON ROAD HUNSTANTON Edge of Town Residential Zone Total No of Dwellings: 17 Survey date: WEDNESDAY 12/09/18	MIXED HOUSES & FLATS	NORFOLK	Survey Type: DIRECTIONAL ATC COUNT
12	SC-03-A-10 GUILDFORD ROAD ASH Neighbourhood Centre (PPS6 Local Centre) Village Total No of Dwellings: 32 Survey date: WEDNESDAY 14/09/22	MIXED HOUSES	SURREY	Survey Type: MANUAL
13	SE-03-A-01 MANOR ROAD NEAR SHEFFIELD WALES Neighbourhood Centre (PPS6 Local Centre) Village Total No of Dwellings: 25 Survey date: THURSDAY 10/09/20	DETACHED & BUNGALOWS	SHEFFIELD	Survey Type: MANUAL
14	SF-03-A-08 STANNINGFIELD ROAD NEAR BURY ST EDMUNDS GREAT WHELNETHAM Neighbourhood Centre (PPS6 Local Centre) Village Total No of Dwellings: 34 Survey date: WEDNESDAY 16/09/20	MIXED HOUSES	SUFFOLK	Survey Type: MANUAL
15	ST-03-A-08 SILKMORE CRESCENT STAFFORD MEADOWCROFT PARK Edge of Town Residential Zone Total No of Dwellings: 26 Survey date: WEDNESDAY 22/11/17	DETACHED HOUSES	STAFFORDSHIRE	Survey Type: MANUAL

This section provides a list of all survey sites and days in the selected set. For each individual survey site, it displays a unique site reference code and site address, the selected trip rate calculation parameter and its value, the day of the week and date of each survey, and whether the survey was a manual classified count or an ATC count.

TRIP RATE for Land Use 03 - RESIDENTIAL/A - HOUSES PRIVATELY OWNED

TOTAL VEHICLES

Calculation factor: 1 DWELLS

BOLD print indicates peak (busiest) period

Time Range	ARRIVALS			DEPARTURES			TOTALS		
	No. Days	Ave. DWELLS	Trip Rate	No. Days	Ave. DWELLS	Trip Rate	No. Days	Ave. DWELLS	Trip Rate
00:00 - 01:00									
01:00 - 02:00									
02:00 - 03:00									
03:00 - 04:00									
04:00 - 05:00									
05:00 - 06:00									
06:00 - 07:00									
07:00 - 08:00	15	25	0.072	15	25	0.293	15	25	0.365
08:00 - 09:00	15	25	0.181	15	25	0.396	15	25	0.577
09:00 - 10:00	15	25	0.152	15	25	0.266	15	25	0.418
10:00 - 11:00	15	25	0.152	15	25	0.186	15	25	0.338
11:00 - 12:00	15	25	0.234	15	25	0.168	15	25	0.402
12:00 - 13:00	15	25	0.207	15	25	0.205	15	25	0.412
13:00 - 14:00	15	25	0.221	15	25	0.215	15	25	0.436
14:00 - 15:00	15	25	0.170	15	25	0.207	15	25	0.377
15:00 - 16:00	15	25	0.309	15	25	0.197	15	25	0.506
16:00 - 17:00	15	25	0.311	15	25	0.165	15	25	0.476
17:00 - 18:00	15	25	0.340	15	25	0.199	15	25	0.539
18:00 - 19:00	15	25	0.311	15	25	0.162	15	25	0.473
19:00 - 20:00									
20:00 - 21:00									
21:00 - 22:00									
22:00 - 23:00									
23:00 - 24:00									
Total Rates:			2.660			2.659			5.319

This section displays the trip rate results based on the selected set of surveys and the selected count type (shown just above the table). It is split by three main columns, representing arrivals trips, departures trips, and total trips (arrivals plus departures). Within each of these main columns are three sub-columns. These display the number of survey days where count data is included (per time period), the average value of the selected trip rate calculation parameter (per time period), and the trip rate result (per time period). Total trip rates (the sum of the column) are also displayed at the foot of the table.

To obtain a trip rate, the average (mean) trip rate parameter value (TRP) is first calculated for all selected survey days that have count data available for the stated time period. The average (mean) number of arrivals, departures or totals (whichever applies) is also calculated (COUNT) for all selected survey days that have count data available for the stated time period. Then, the average count is divided by the average trip rate parameter value, and multiplied by the stated calculation factor (shown just above the table and abbreviated here as FACT). So, the method is: $COUNT/TRP*FACT$. Trip rates are then rounded to 3 decimal places.

The survey data, graphs and all associated supporting information, contained within the TRICS Database are published by TRICS Consortium Limited ("the Company") and the Company claims copyright and database rights in this published work. The Company authorises those who possess a current TRICS licence to access the TRICS Database and copy the data contained within the TRICS Database for the licence holders' use only. Any resulting copy must retain all copyrights and other proprietary notices, and any disclaimer contained thereon.

The Company accepts no responsibility for loss which may arise from reliance on data contained in the TRICS Database. [No warranty of any kind, express or implied, is made as to the data contained in the TRICS Database.]

Parameter summary

Trip rate parameter range selected: 12 - 34 (units:)
 Survey date range: 01/01/16 - 18/09/24
 Number of weekdays (Monday-Friday): 15
 Number of Saturdays: 0
 Number of Sundays: 0
 Surveys automatically removed from selection: 0
 Surveys manually removed from selection: 0

This section displays a quick summary of some of the data filtering selections made by the TRICS® user. The trip rate calculation parameter range of all selected surveys is displayed first, followed by the range of minimum and maximum survey dates selected by the user. Then, the total number of selected weekdays and weekend days in the selected set of surveys are shown. Finally, the number of survey days that have been manually removed from the selected set outside of the standard filtering procedure are displayed.